



北京市规划和国土资源管理委员会 建设项目规划条件

(土地储备供应)
(海淀分局)

2018规土(海)条供字0002号

制作日期: 2018年11月13日

北京市土地整理储备中心海淀区分中心:

你单位2018年10月15日申报拟上市供应的用地位于海淀区安宁庄东路1号有关材料收悉。经研究,按照政府土地储备供应计划的安排,根据有关法律、法规、规章的规定和城乡规划要求,提供该地块的规划条件作为供地的规划依据。

●土地储备供应用地及建设规划要求:

△土地储备供应用地位置、范围:(详见附件)

该项目用地位于海淀区清河地区,东至安宁庄东路,南至现状安宁华庭小区,西至安宁庄西路,北至安宁庄路。

△土地储备供应用地的规划地块编号、用地性质、用地规模、容积率、地上建筑规模、控制高度、建筑密度、绿地率等详见下表:

各地块规划指标								
序号	规划地块编号	用地性质	用地规模 (平方米)	容积率	地上建筑规模 (平方米)	控制高度 (米)	建筑密度 (%)	绿地率 (%)
1	1820-618	R2二类居住用地	27000	2.5	67500	60	30	30
2	1820-619	R2二类居住用地	48600	2	97200	45	30	30
3	1820-620	A33基础教育用地	17100	0.8	13680	20	30	30
4	1820-622	A33基础教育用地	5100	0.8	4080	12	40	30
5	1820-624	R2二类居住用地	25900	2.5	64750	60	30	30
6	1820-625	A8社区综合服务设施用地	6000	1	6000	12	50	30
7	1820-626	S32公交场站设施用地	2000	0.4	800	12	30	35
8	1820-627	U17邮政设施用地	2000	1	2000	12	40	30
小计	——	——	133700	——	256010	——	——	——

△总用地规模: 189374.93平方米

△总建设用地规模: 约133700平方米(准确数字以拨地钉桩成果为准)

△依土地储备工作实施要求,在供应上述用地的同时,须同步实施以下用地性质明确的相关内容:

序号	规划地块编号	用地性质	用地规模约 (平方米)	备注
1	1820-617	G1公园绿地	5700	/
2	1820-621	G1公园绿地	10800	/
3	1820-623	G1公园绿地	1000	/
4		S1城市道路用地	38174.93	/
小计		——	55674.93	

●建设规划要求:

△建筑退让距离:

□应满足北京市人民政府《关于在城市道路两侧和交叉路口周围新建、改建建筑工程的若干规定》和《北京地区建设工程规划设计通则》的要求。

△建筑间距:

□应符合《北京市生活居住建筑间距暂行规定》以及日照、消防等要求。

△装配式建筑:

□本项目应按照《北京市人民政府办公厅关于加快发展装配式建筑的实施意见》（京政办发【2017】8号）及市住建委的有关要求，全部采用装配式建筑。

●环境设计要求:

△建筑立面（色彩、造型）：与周边建筑相协调

●绿化环境规划要求:

△绿地率：≥35%（1820-618、1820-619、1820-620、1820-622、1820-624、1820-625、1820-627地块≥30%，1820-626地块≥35%）

△古树名木保护：应符合《北京市古树名木保护管理条例》的要求。

△其他树木要求：胸径30厘米以上的树木应当予以保留，如需移伐须取得园林绿化主管部门意见。

●交通规划要求:

△与外部交通衔接的主要出入口方位：结合交通影响评价确定，具体以审定方案为准

△停泊车位:

□应满足《北京市居住公共服务设施配置指标》和《北京市居住公共服务设施配置指标实施意见》（京政发【2015】7号）、《北京市城市建设节约用地标准》（试行）以及《北京地区建设工程规划设计通则》（2003年试行）的有关规定。

●市政基础设施规划要求:

△根据项目建设需求，商各相关行业部门落实供水、供电、供热、供燃气、雨水、污水、再生水、信息管线等市政基础设施条件。

●文物保护要求:

△地下文物保护要求:

□按照《北京市地下文物保护管理办法》（市政府令第251号）第十一条规定，对于符合本办法第九条规定的“（一）位于地下文物埋藏区；（二）旧城之内建设项目总用地面积一万平方米以上；（三）旧城之外建设项目总用地面积二万平方米以上；（四）法律、法规和规章规定的其他情况”的土地储备开发项目，承担土地储备任务的单位应当按照本市规定报请市文物行政管理部门组织考古发掘单位进行考古调查、勘探。

考古调查、勘探工作完成后，考古发掘单位应当出具是否具备入市交易条件的意见，相关意见作为土地入市交易的依据之一。

●居住项目规划设计要求及公共服务设施配建要求:

△设计方案中应安排太阳能热水装置。

△多层居住建筑应采用坡屋顶形式。

△建设项目应采用绿色照明技术、供暖锅炉系统节能技术、空调系统节能技术、电机系统节能技术、高温空气燃烧技术、热泵技术、太阳能利用技术、雨洪利用技术、节水器具及节水控制技术等节能节水、减排技术，并在设计说明中做出专门说明。

△凡本市行政区域内新建、改建、扩建和翻建四层（含）以上住宅的，均须进行适老性设计。

住宅适老性设计具体内容包括：设置电梯、紧急呼叫装置、安装扶手等。各设计单位在进行住宅项目适老性设计时，除符合国家及本市相关技术标准规范外，在设计说明中须注明电梯规格、位置，并在设计中预留设置紧急呼叫装置和安装扶手的条件。

△对既有住宅楼外部增设电梯时，对于井道和轿厢壁采用透明材料，且电动机设备不放在顶部的，建筑间距在满足“两建筑长边相对的不小于18米、一建筑的长边与另一建筑的端边相对的不小于12米、两建筑的端边相对的不小于10米”和消防要求的情况下即可设置。除此类外部增设电梯的情况外，均应符合国家和本市建筑间距和日照相关规定。

△项目建设应按照《北京市居住公共服务设施配置指标实施意见》（京政发〔2015〕7号）的要求，落实居住项目公共服务设施的配置、补充和完善工作。按照“查漏补缺、先批设施、后批住宅”的原则，确保街区级、社区级居住公共服务设施与住宅建设同步实施，其中社区综合管理服务类、教育类、医疗卫生类公共服务设施应在住宅总规模完成50%前，其他公共服务设施应在住宅总规模完成80%前完成建设，并同步验收、同步交付使用。

对分期、分区域建设的，要合理安排建设时序，确保建设项目级居住公共服务设施在住宅总规模完成80%前完成建设，并同步验收。未按照时序建设、验收、交付居住公共服务设施的，规划部门可对竣工的住宅建设工程不予规划核验，并对该建设项目其他建设工程暂缓核发规划许可；住房城乡建设部门不予办理竣工验收备案手续。

●其他：

△其他要求：

1、关于规划指标方面的要求：地上建筑规模、控高、建筑密度为上限，绿地率为下限。住宅建筑标准层层高一般不应超过3.3米。按照《关于北京市海淀区18片区1814、1820街区部分地块（西三旗建材城中路东侧地块、清河安宁庄东路1号地块）控制性详细规划的批复》（市规划国土函[2018]2777号）中分供地方方案示意图的有关要求，1820-618A地块居住用地1.23公顷，1820-618B地块居住用地1.47公顷（1820-618地块统一核算规划指标）；1820-619A地块居住用地3.02公顷，1820-619B地块居住用地1.84公顷，含一处用地规模约1500平方米的密闭式垃圾分类收集站（1820-619地块统一核算规划指标）；1820-624A地块居住用地0.89公顷，1820-624B地块居住用地1.7公顷（1820-624地块统一核算规划指标）；1820-620地块小学用地为24班小学，用地布局可结合方案进行优化；1820-622地块托幼用地为12班托幼，用地布局可结合方案进行优化；1820-625地块社区综合服务设施用地含社区卫生服务设施和养老服务设施，1820-626地块的公交场站设施用地为公交首末站。

2、按照相关法律法规规章的规定，应充分征求储备整理用地范围内现有土地使用权人意见，进一步做好土地前期整理工作。

3、关于公共服务设施方面的要求：应按照市政府《关于印发〈北京市居住公共服务设施配置指标〉和〈北京市居住公共服务设施配置指标实施意见〉的通知》（京政发〔2015〕7号）的有关要求，进一步明确公共服务设施的投资主体和同步实施方案，并依据《北京市新建商品住宅小区住宅与市政公共基础设施、公共服务设施同步交付使用管理暂行办法》（京建法〔2007〕99号）要求建设。

4、关于雨水工程利用方面的要求：应按照市规划委《关于加强建设工程用地内雨水资源利用的暂行规定》（市规发〔2003〕258号）、《关于加强雨水利用工程规划管理有关事项的通知》（市规发〔2012〕791号）及《雨水控制与利用工程设计规范（DB11/685-2013）》的有关要求。下一步提交的建设工程设计方案总平面图中，对雨水利用工程的设计情况进行说明，明确标注采用透水铺装面积的比例，雨水调蓄设施的规模、位置等内容。

5、关于绿色建筑方面的要求：应遵照北京市政府《关于全面发展绿色建筑推动生态城市建设的意见》的有关要求以及市住建委等十一个委办局联合发布的《关于在本市保障性住房中实施绿色建筑行动的若干指导意见》（京建发〔2014〕315号）执行。

6、关于公用充电设施方面的要求：应按照市发展改革委、市科委、市规划委等4个部门《关于印发北京市新能源小客车公用充电设施投资建设管理办法（试行）的通知》（市发改规[2015]2号）的有关要求建设充电设施或预留建设安装条件。

7、关于项目规划道路、绿地等同步实施公共用地的要求：根据市规划国土委《关于对涉及2018年住宅供地计划的部分用地控规进行优化调整的请示》（市规划国土文[2018]437号）的有关要求，建议海淀区政府在实施过程中，统筹安排好建设时序，随项目同步实施建设用地内的公共服务设施、交通和市政基础设施，同步实施规划绿地；同步实施地块及周边城市支路、配套小学和幼儿园及市政基础设施。

8、关于节能方面的要求：本项目应优化建筑设计，统筹考虑能源供应及利用方案，选用高效节能环保设备，鼓励使用可再生能源，完善能源管理措施，提升绿色建筑星级及占比，控制能源消费总量及碳排放数量。

9、关于停车泊位的要求：应满足《北京市居住公共服务设施配置指标》和《北京市居住公共服务设施配置指标实施意见》（京政发[2015]7号）、《北京市城市建设节约用地标准》（试行）及《北京地区建设工程规划设计通则》（2003年试行）的有关规定，并结合交通影响评价确定，最终以审定设计方案为准。

10、关于装配式建筑的要求：本项目应按照《北京市人民政府办公厅关于加快发展装配式建筑的实施意见》（京政办发〔2017〕8号）及市住房城乡建设行政主管部门的相关要求执行。

11、下一步应就交通、环保、民防、抗震、文物、人防、水务等事宜征求、执行相关管理部门意见。

告知事项：

1、本建设项目规划条件（土地储备供应）有效期与国有建设用地使用权出让合同有效期一致。


2、本《建设用地规划条件（土地储备供应）》含附图（用地范围图——机打彩图），文图一体方为有效文件。

3. 本《建设项目规划条件（土地储备供应）》（含附图）一式6份（含抄送建设计划主管部门一份），文图一体方为有效文件。

抄送单位： 市园林绿化局、市文物局

北京市规划和国土资源管理委员会
建设项目规划条件附图
(土地储备供应)

比例尺 1:5000

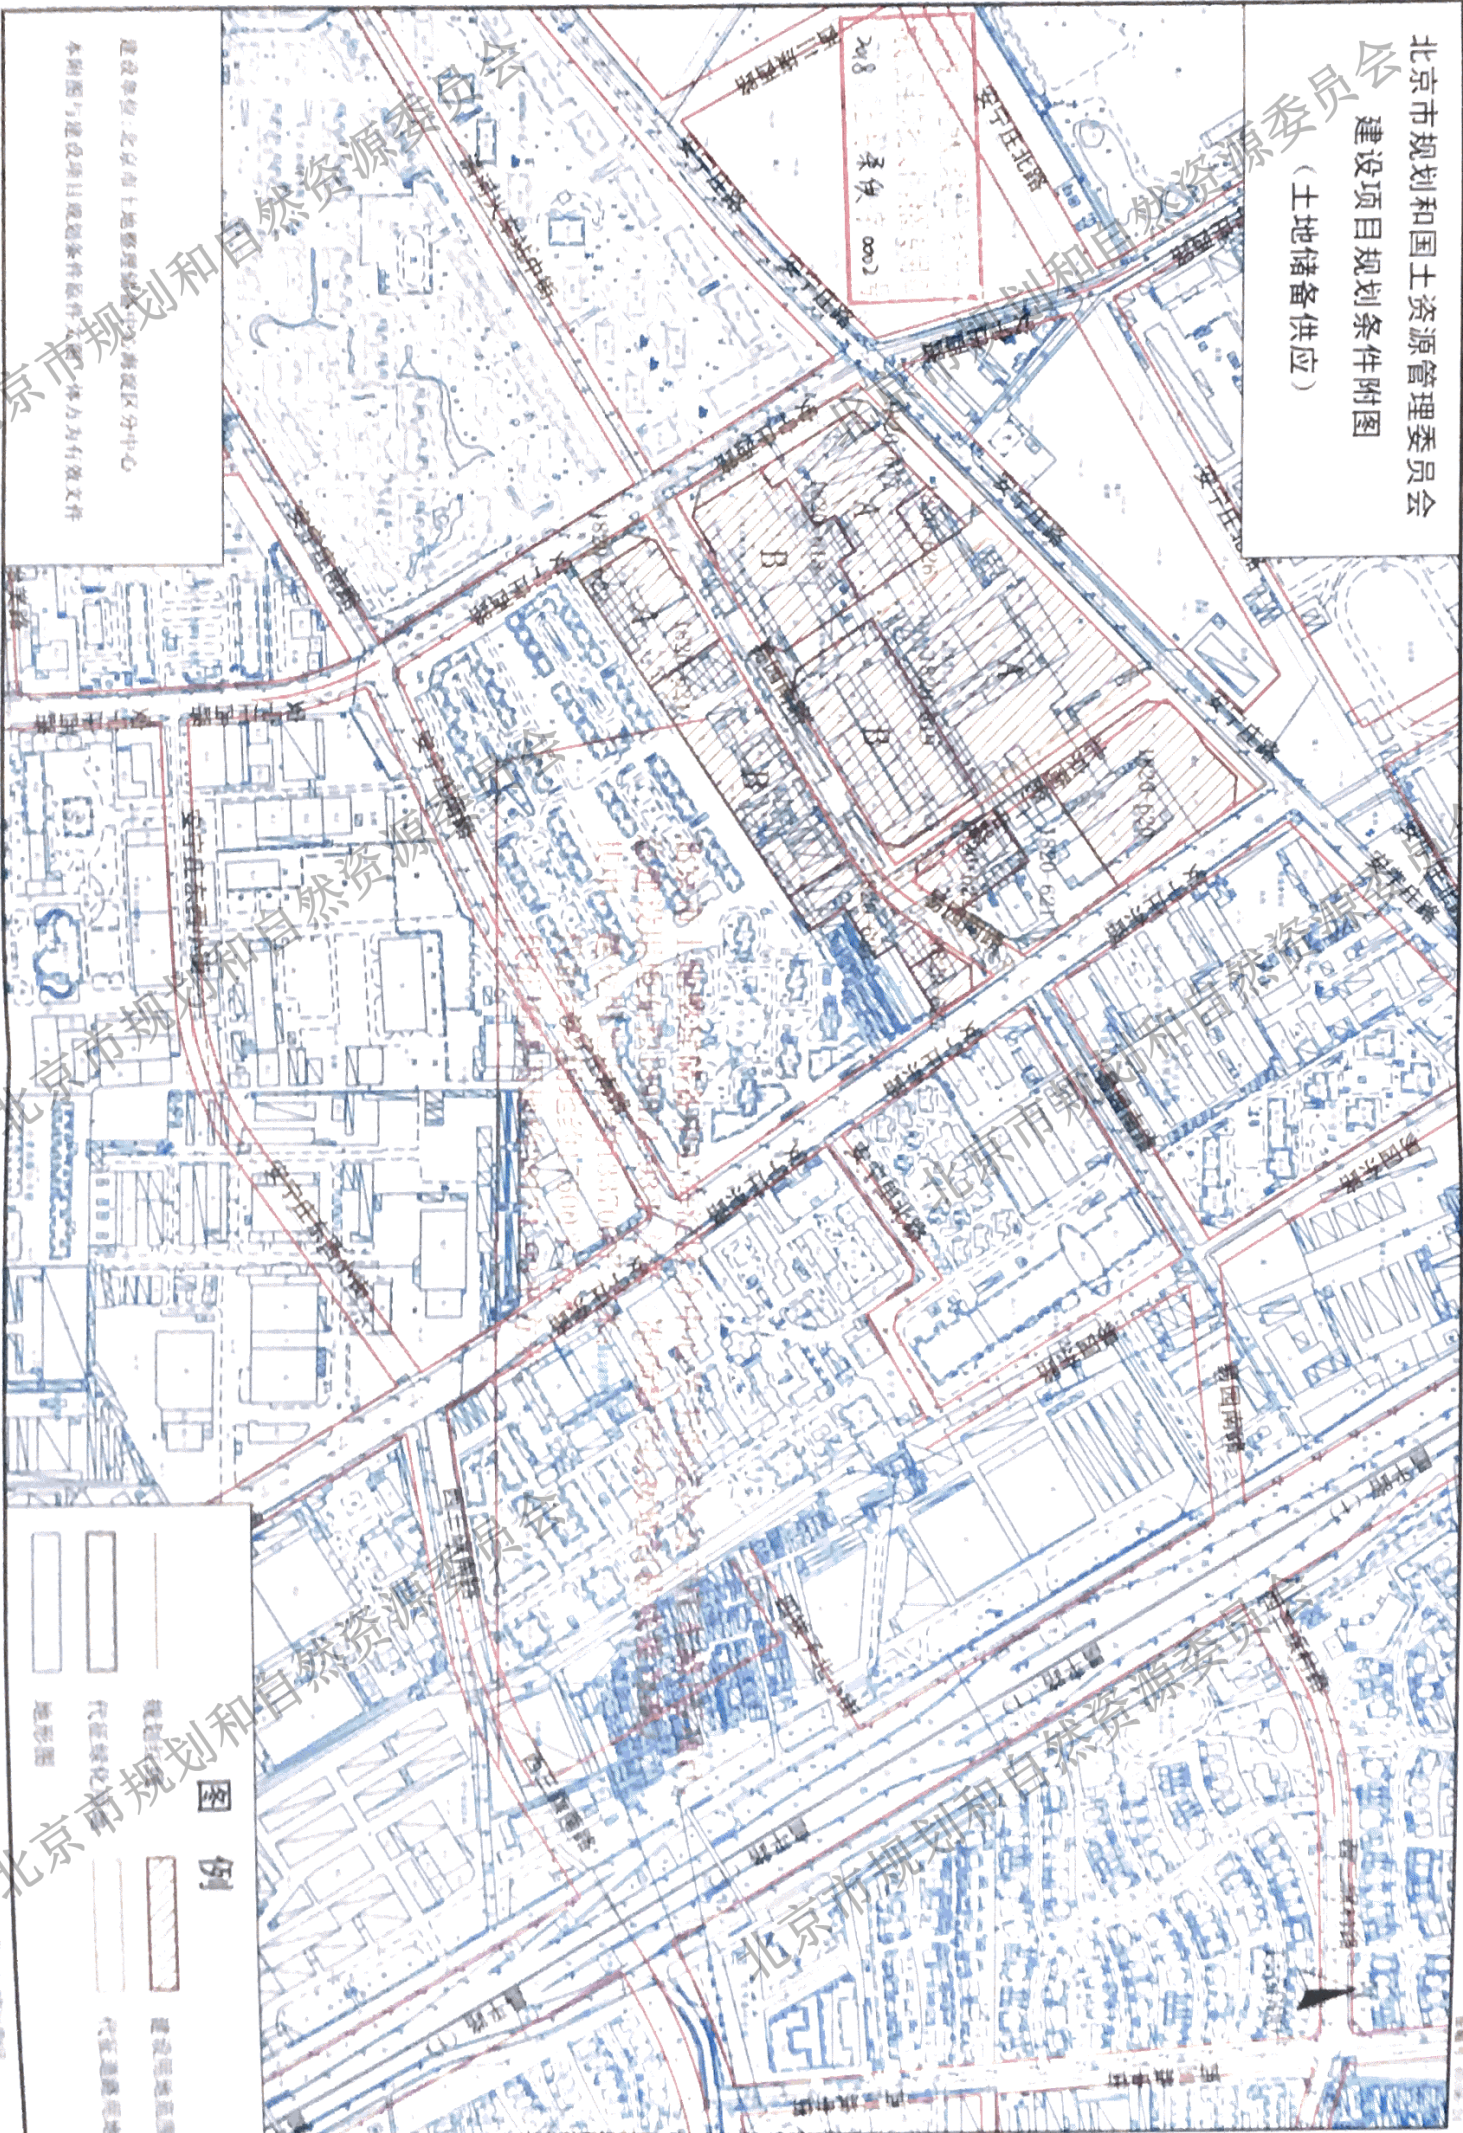

建设单位: 北京市规划和国土资源管理委员会

本附图与建设项目规划条件附件具有同等法律效力

图例

比例尺 1:5000

北京市规划和国土资源管理委员会

北京市规划和国土资源管理委员会
建设项目规划条件附图
(土地储备供应)

